






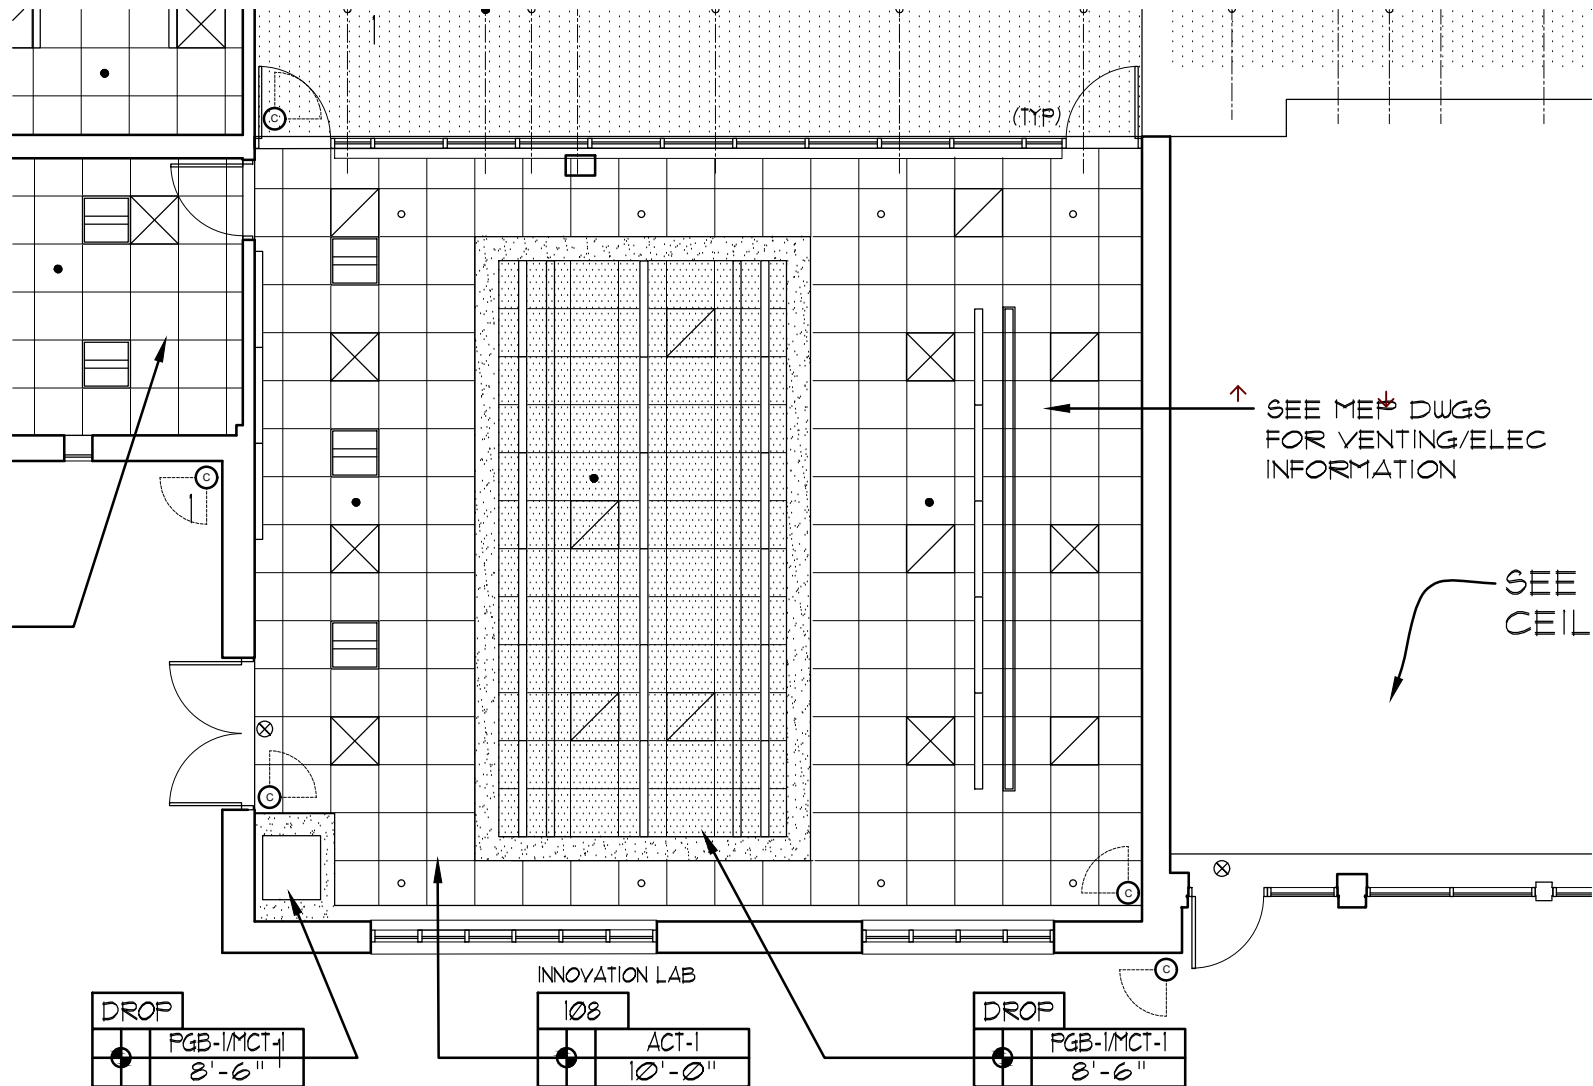


KSUS INNOVATION LAB
REFLECTED CEILING PLAN
PGA 250825

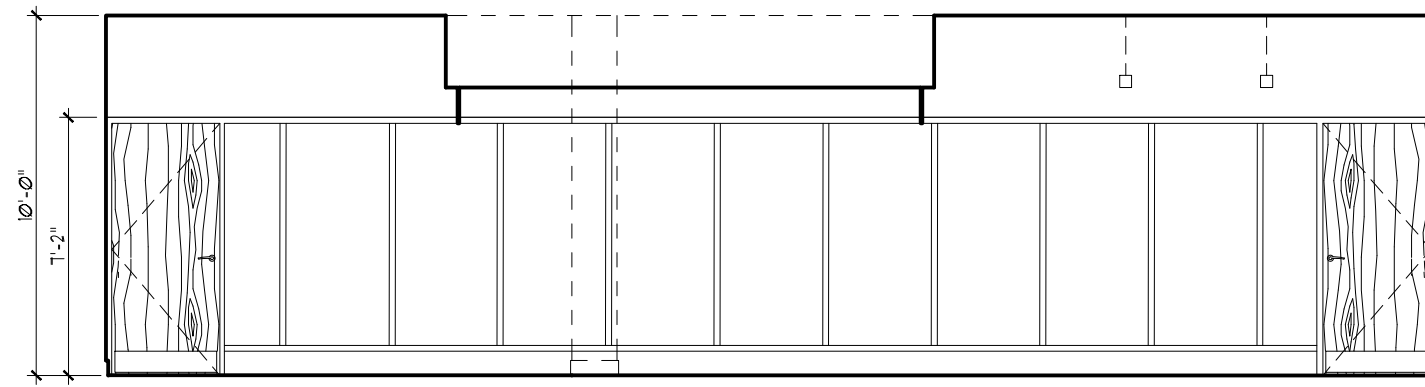


1 INTERIOR ELEVATION
INNOVATION LAB #108 SCALE: 1/4"=1'-0"

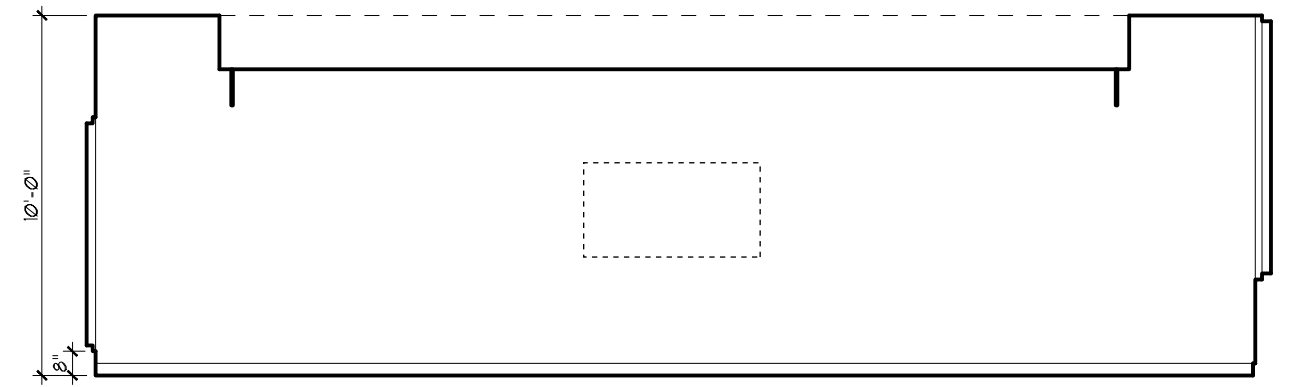

2 INTERIOR ELEVATION
INNOVATION LAB #108 SCALE: 1/4"=1'-0"

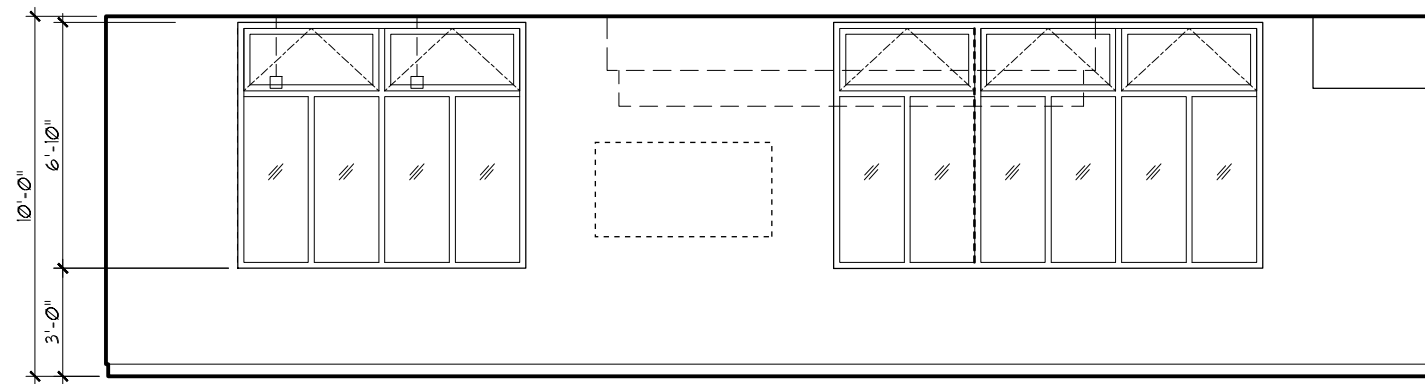

3 INTERIOR ELEVATION
INNOVATION LAB #108 SCALE: 1/4"=1'-0"

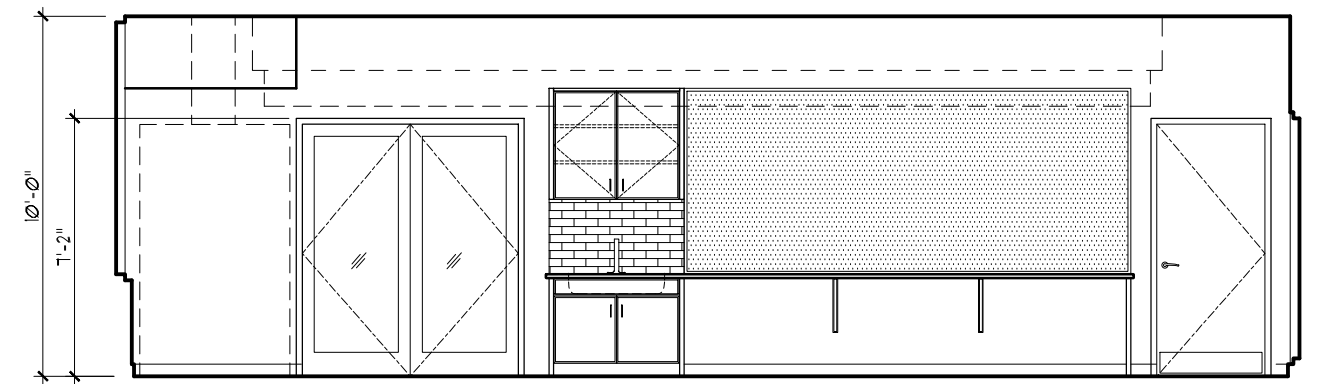

4 INTERIOR ELEVATION
INNOVATION LAB #108 SCALE: 1/4"=1'-0"

KSUS INNOVATION LAB
INTERIOR ELEVATIONS
PGA 250825