


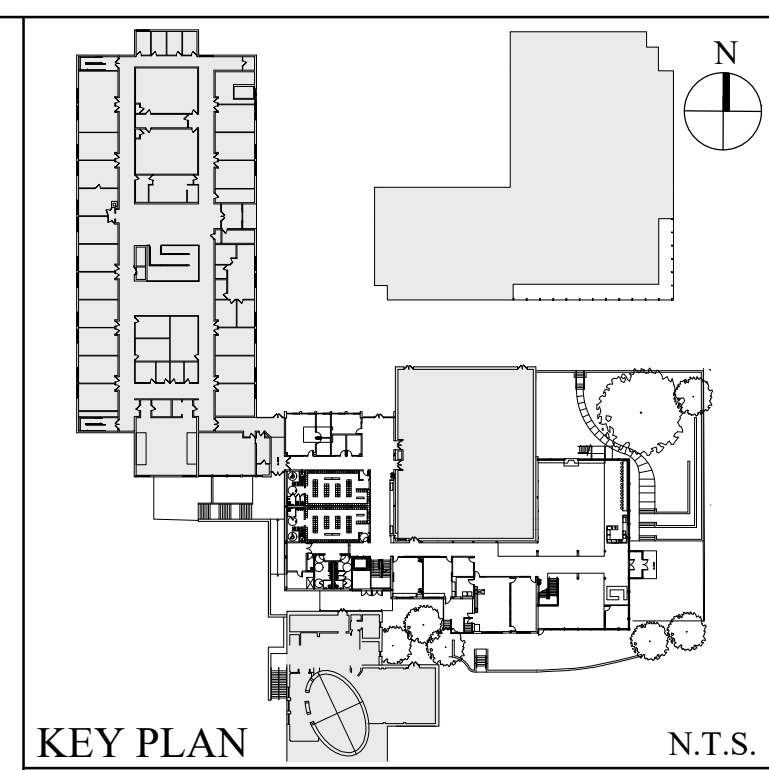

KEY PLAN N.T.S.

NOT FOR CONSTRUCTION

5.	08/29/2025	ISSUE FOR BID
4.	06/30/2025	100% CD COMPLETE
3.	03/12/2025	50% CD COMPLETE - ADDENDUM 2
2.	02/18/2025	50% CD COMPLETE - ADDENDUM 1
1.	02/07/2025	50% CD COMPLETE - ISSUED FOR CD ESTIMATE

No.	Date	Revision
ARCHITECT		STRUCTURAL ENGINEER
606 GROSSI ASSOCIATES, LLP		DUPILLA CONSULTING ENGINEERS
566 WARDEN AVENUE		1431 MAIN STREET
HOUSTON, TEXAS 77002-3000		HOUSTON, TEXAS 77002
TEL: (713) 494-8737		(713) 495-7737
MEP ENGINEERS		ROOFING CONSULTANT
THOMAS YENKINS, PLLC		WICKS & COMPANY
68 PURCHASE STREET		20 MADISON AVENUE
815		VALHALLA, NY 10989
TEL: (914) 460-9509		(914) 494-3450
CODE CONSULTANT		CONSTRUCTION SPECIFICATIONS INC.
10000 WILSON DRIVE, GLEN AVE		PO BOX 488
241 MAIN STREET SOUTH		212 FIRST STREET
WOODBRURY, CT 06798		MORGANVILLE, NJ 07751
TEL: (203) 271-0754		(732) 979-0700
GEOTECHNICAL ENGINEER (BY OWNER)		CIVIL ENGINEER (BY OWNER)
LUNGAN & CO		RETINUED AND REDESIGNED
555 LONG WILLOW DRIVE		STAMFORD, CT 06905
NEW HAVEN, CT 06505		(203) 377-6906

	Q000J20A-0778	Q000J20A-0799
--	---------------	---------------

Project Title

KING SCHOOL

UPPER SCHOOL
CRI/COMMONS
ADDITION PROJECT

1450 Newfield Avenue
Stamford, CT 06905


Drawing Title _____

UPPER SCHOOL
FIRST FLOOR CONST. PLAN


Scale	Job No.	Date	Drawing No.
	2301.00	02/2025	A-101
Drawn	Checked	Approved	

Peter Gisolfi Associates
Architects • Landscape Architects, LLP
566 Warburton Avenue
Hastings on Hudson, NY 10706
(914) 478-3677

PETER GISOLFI ASSOCIATES LLP

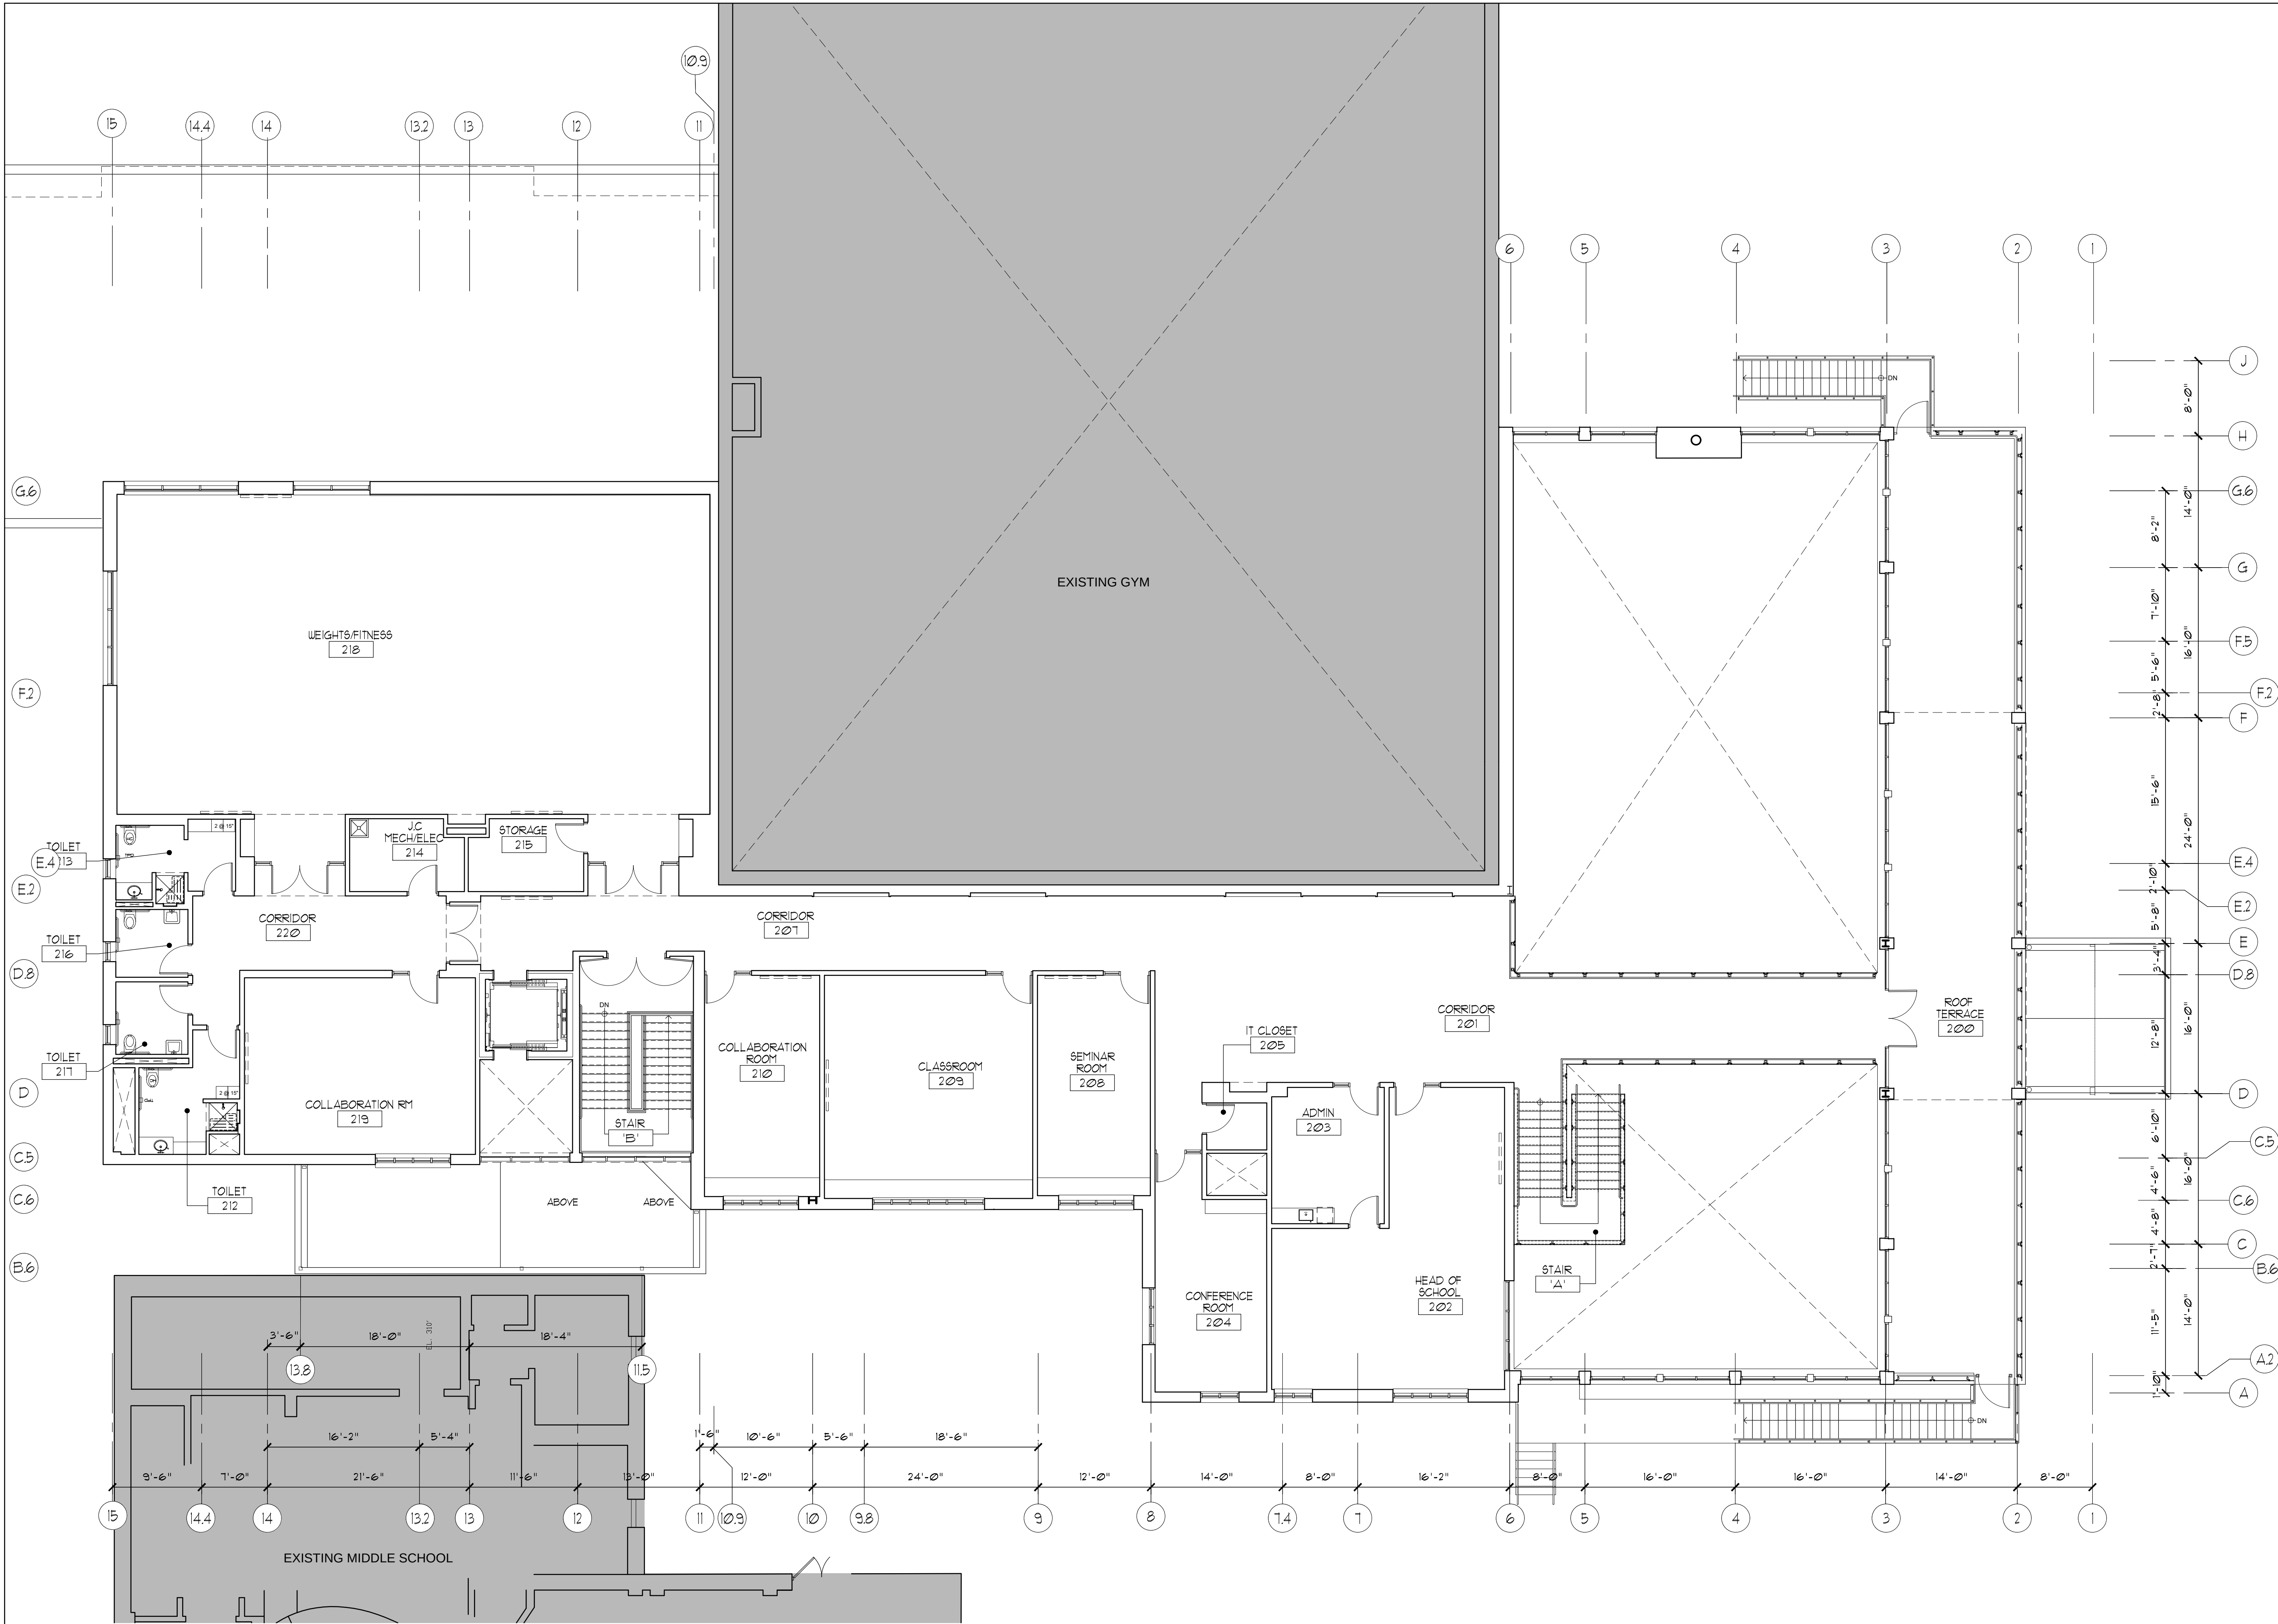


1 UPPER SCHOOL-SECOND FLOOR CONSTRUCTION PLAN
SCALE: 1/8"=1'-0"

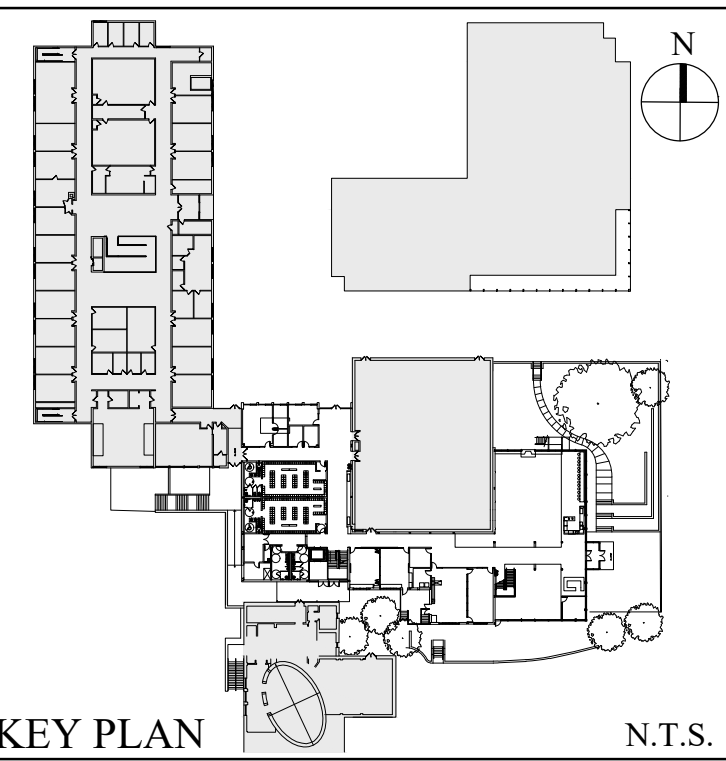


NOT FOR CONSTRUCTION

1. 08/29/2025 ZBA SUBMITTAL		
No.	Date	Revision
ARCHITECT PETER GISOLFI ASSOCIATES, LLP 566 WARBURTON AVENUE HASTINGS-ON-HUDSON, NY 10706 T: (914) 478-3677		
STRUCTURAL ENGINEER DRPILLA CONSULTING ENGINEERS 143 MAIN STREET NYACK, NY 10960 T: (845) 922-7793		
MEP ENGINEERS WATKINS ASSOCIATES 20 MADISON AVENUE VALHALLA, NY 10985 T: (914) 948-3450		
CODE CONSULTANT MILTON GREGORY CREW, AIA 241 MAIN STREET SOUTH WOODBURY, CT 06798 T: (203) 217-1074		
SPECIFICATIONS CONSTRUCTION SPECIFICATIONS INC. PO BOX 488 MORGANVILLE, NJ 07751 T: (732) 970-4700		
GEOTECHNICAL ENGINEER (BY OWNER) LANGAN CT, INC. 555 LONG WHARF DRIVE NEW HAVEN, CT 06595 (203) 562-5771		
CIVIL ENGINEER (BY OWNER) RTDNESS AND MEAD 22 FIRST STREET STAMFORD, CT 06905 (203) 327-0500		
Stamp		
Project Title KING SCHOOL UPPER SCHOOL CRI/COMMONS ADDITION PROJECT 1450 Newfield Avenue Stamford, CT 06905		
Drawing Title SECOND FLOOR CONST. PLAN		
Scale	Job No. 2301.00	Date 02/2025
Drawn	Checked	Approved
Peter Gisolfi Associates Architects • Landscape Architects, LLP 566 Warburton Avenue Hastings-on-Hudson, NY 10706 (914) 478-3677		
PETER GISOLFI ASSOCIATES LLP		
A-102		

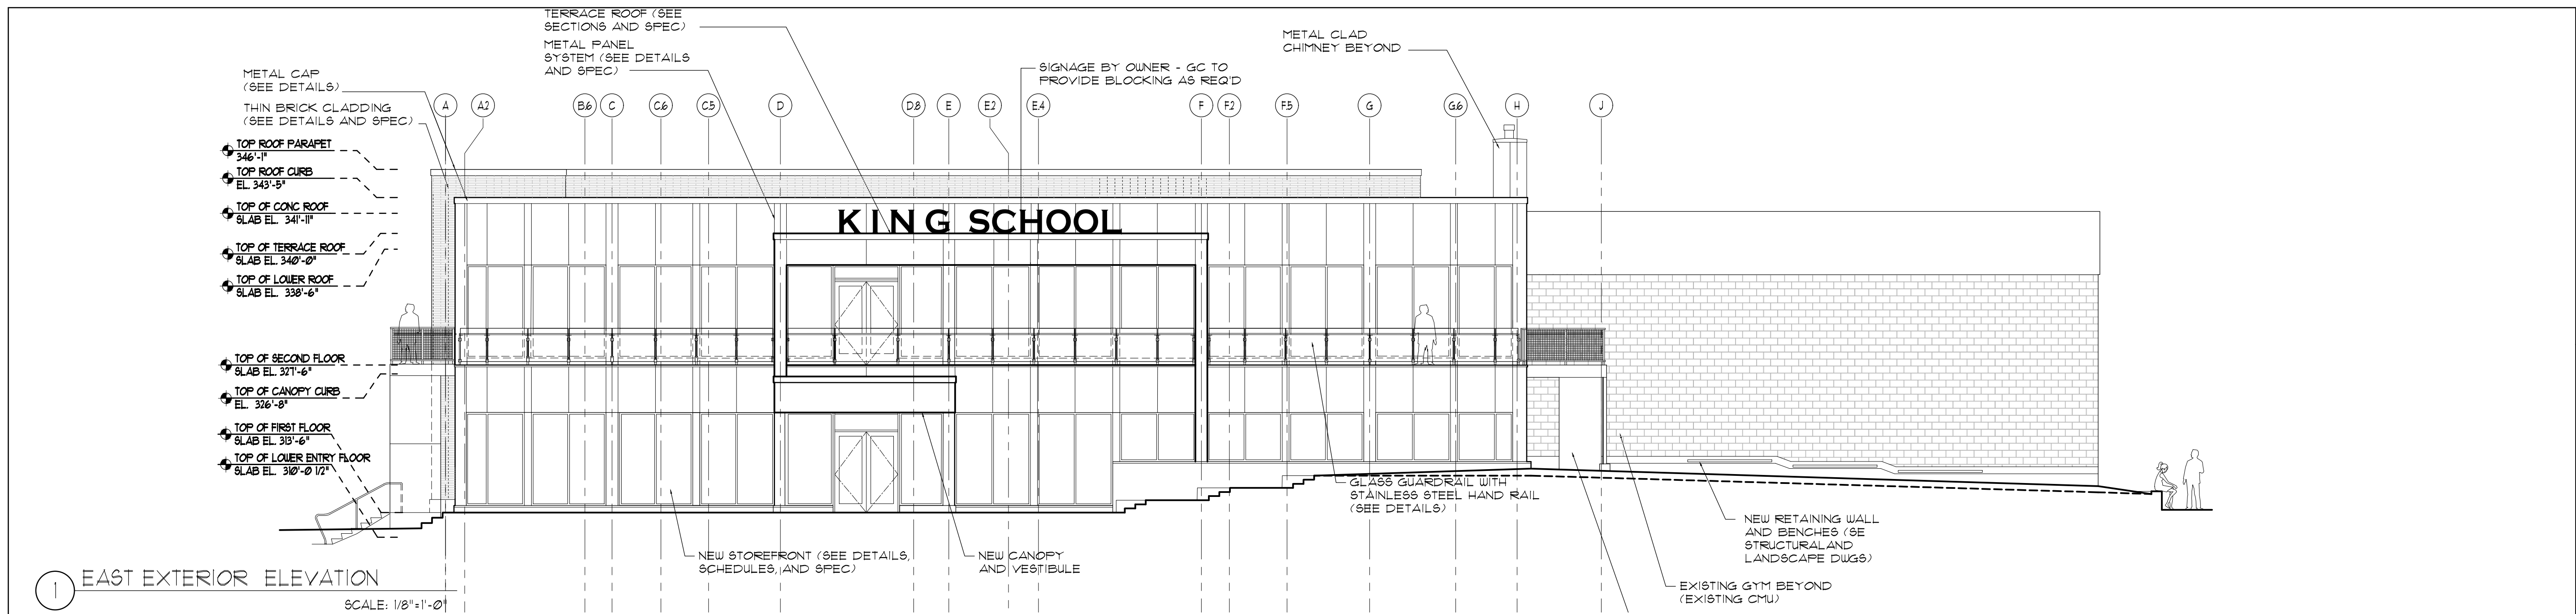


1 EAST EXTERIOR ELEVATION

SCALE: 1/8"=1'-0"

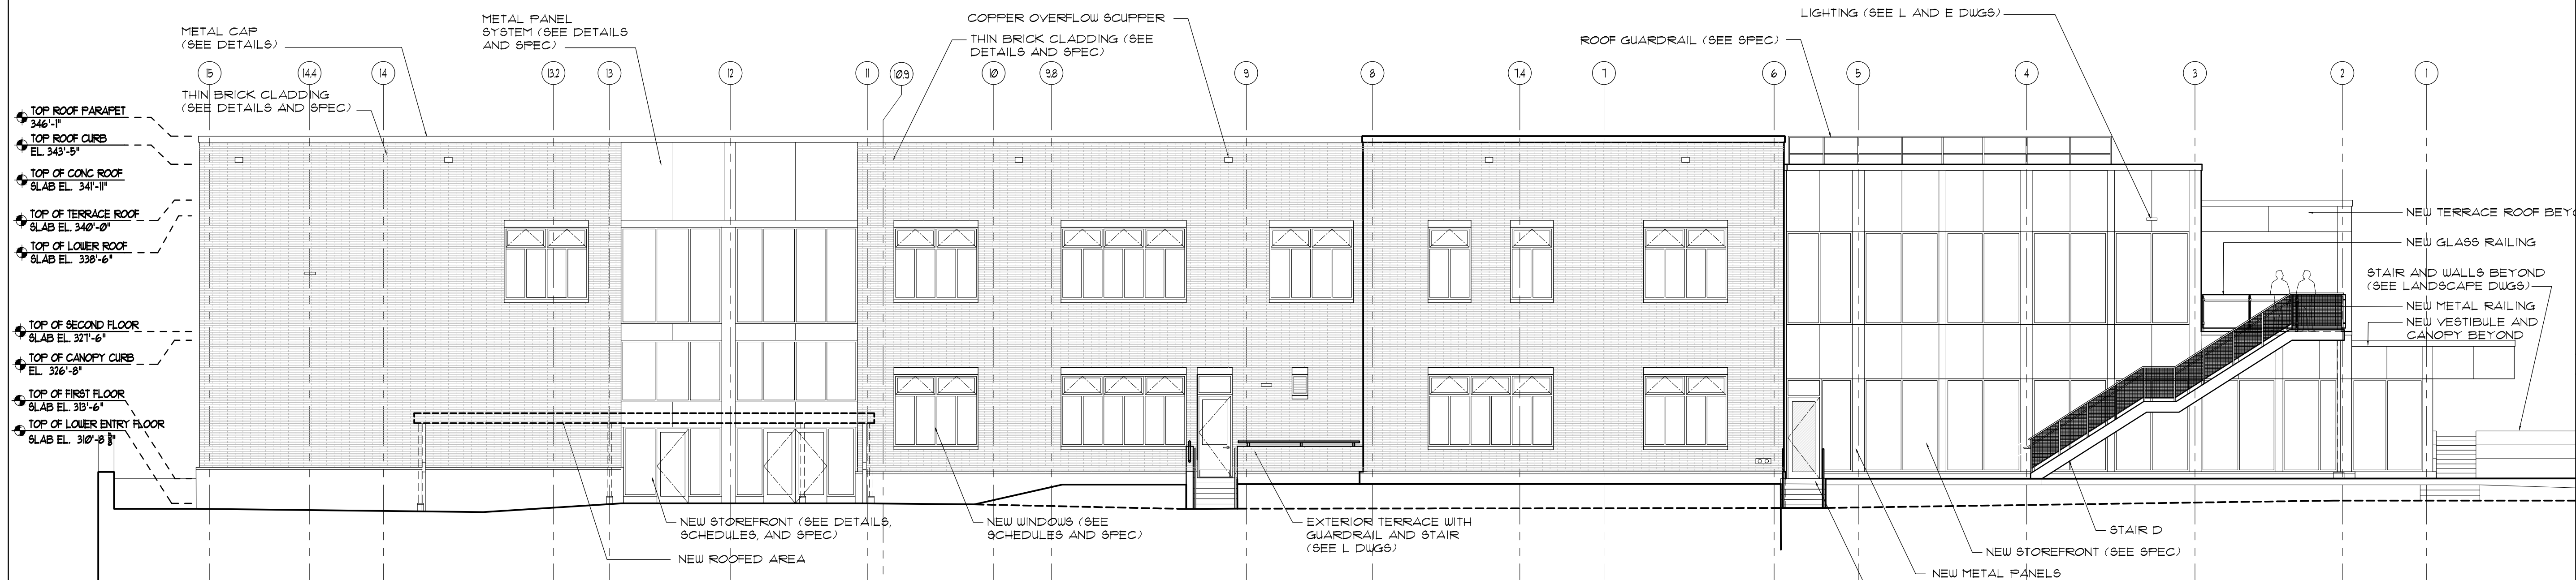


2 SOUTH EXTERIOR ELEVATION

SCALE: 1/8"=1'-0"

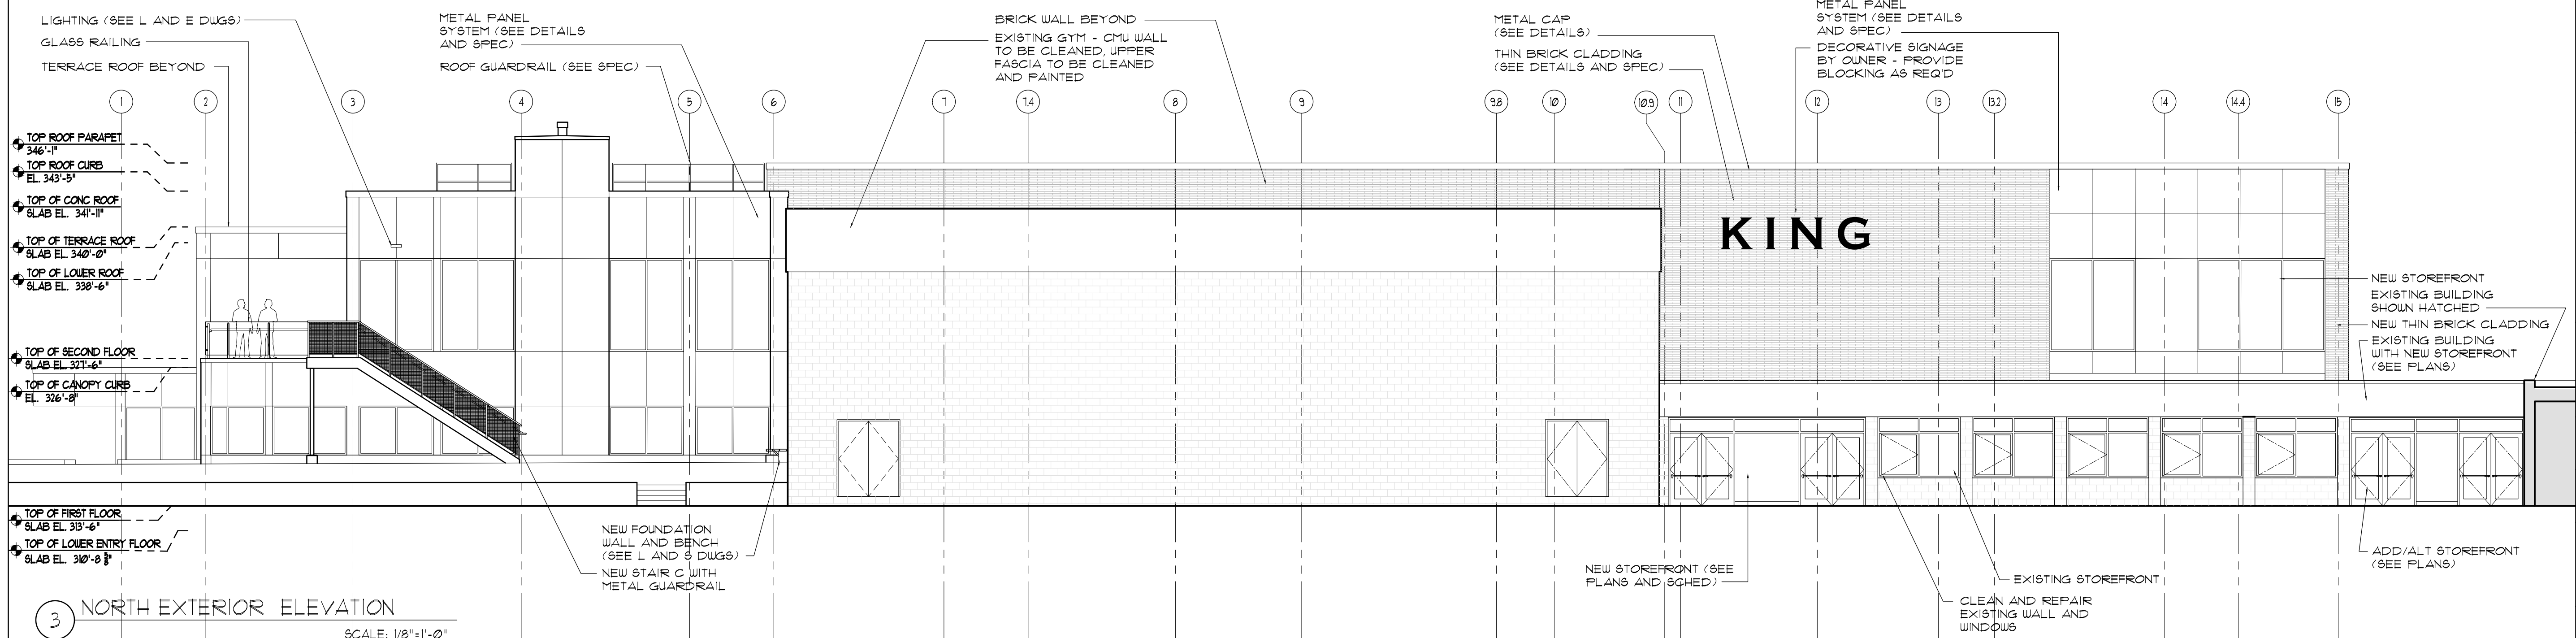


3 NORTH EXTERIOR ELEVATION

SCALE: 1/8"=1'-0"

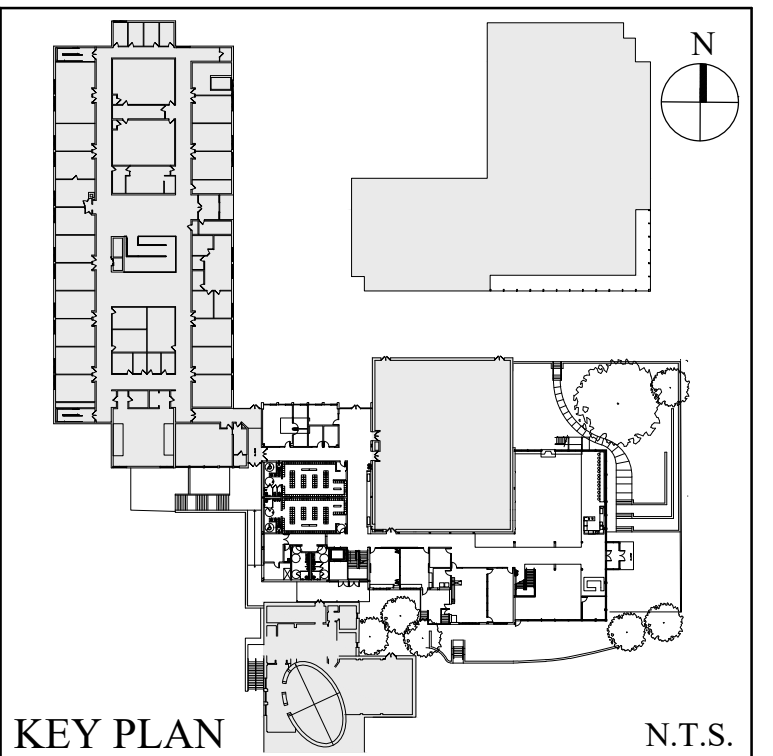


NOT FOR CONSTRUCTION


1. 08/29/2025 ZBA SUBMITTAL			
No.	Date	Revision	
ARCHITECT PETER GISOLFI ASSOCIATES, LLP 566 WARBURTON AVENUE HASTINGS-ON-HUDSON, NY 10706 T: (914) 478-3677			
STRUCTURAL ENGINEER DRPILLA CONSULTING ENGINEERS 143 MAIN STREET NYACK, NY 10960 T: (845) 922-7793			
MEP ENGINEERS TETTER VENGAS, PLLC 68 PURCHASE STREET RYE, NY 10580 T: (914) 967-9509			
ROOFING CONSULTANT WATKINS ASSOCIATES 20 MADISON AVENUE VALHALLA, NY 10985 T: (914) 948-3450			
CODE CONSULTANT MILTON GREGORY CREW, AIA 241 MAIN STREET SOUTH WOODBURY, CT 06798 T: (203) 217-1074			
SPECIFICATIONS CONSTRUCTION SPECIFICATIONS INC. PO BOX 488 MORGANTOWN, NJ 07751 T: (732) 970-0700			
GEOTECHNICAL ENGINEER (BY OWNER) LANGAN CT, INC. 555 LONG WHARF DRIVE NEW HAVEN, CT 06595 (203) 562-5771			
CIVIL ENGINEER (BY OWNER) RTDNESS AND MEAD 22 FIRST STREET STAMFORD, CT 06905 (203) 327-0500			
Stamp			
Project Title KING SCHOOL UPPER SCHOOL CRI/COMMONS ADDITION PROJECT 1450 Newfield Avenue Stamford, CT 06905			
Drawing Title UPPER SCHOOL EXTERIOR ELEVATIONS			
Scale	Job No.	Date	Drawing No.
	2301.00	02/2025	A-200
Drawn	Checked	Approved	
Peter Gisolfi Associates Architects • Landscape Architects, LLP 566 Warburton Avenue Hastings-on-Hudson, NY 10706 (914) 478-3677			
PETER GISOLFI ASSOCIATES LLP			

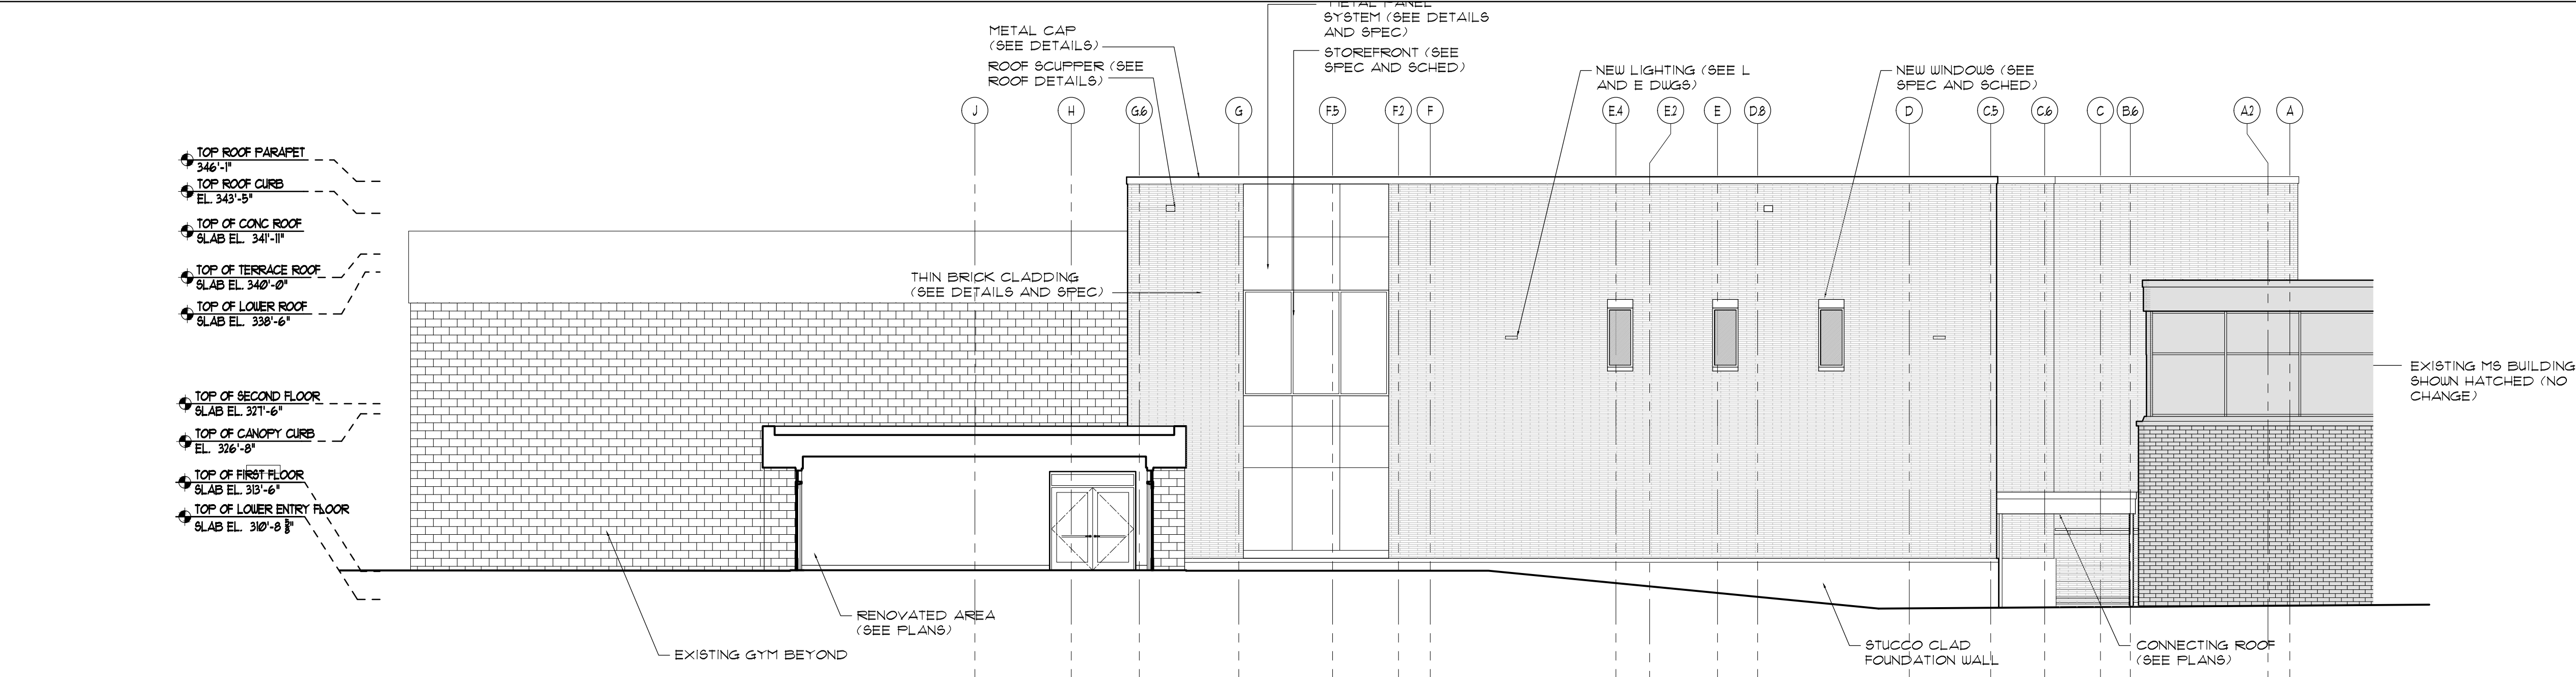


1 WEST EXTERIOR ELEVATION
SCALE: 1/8"=1'-0"

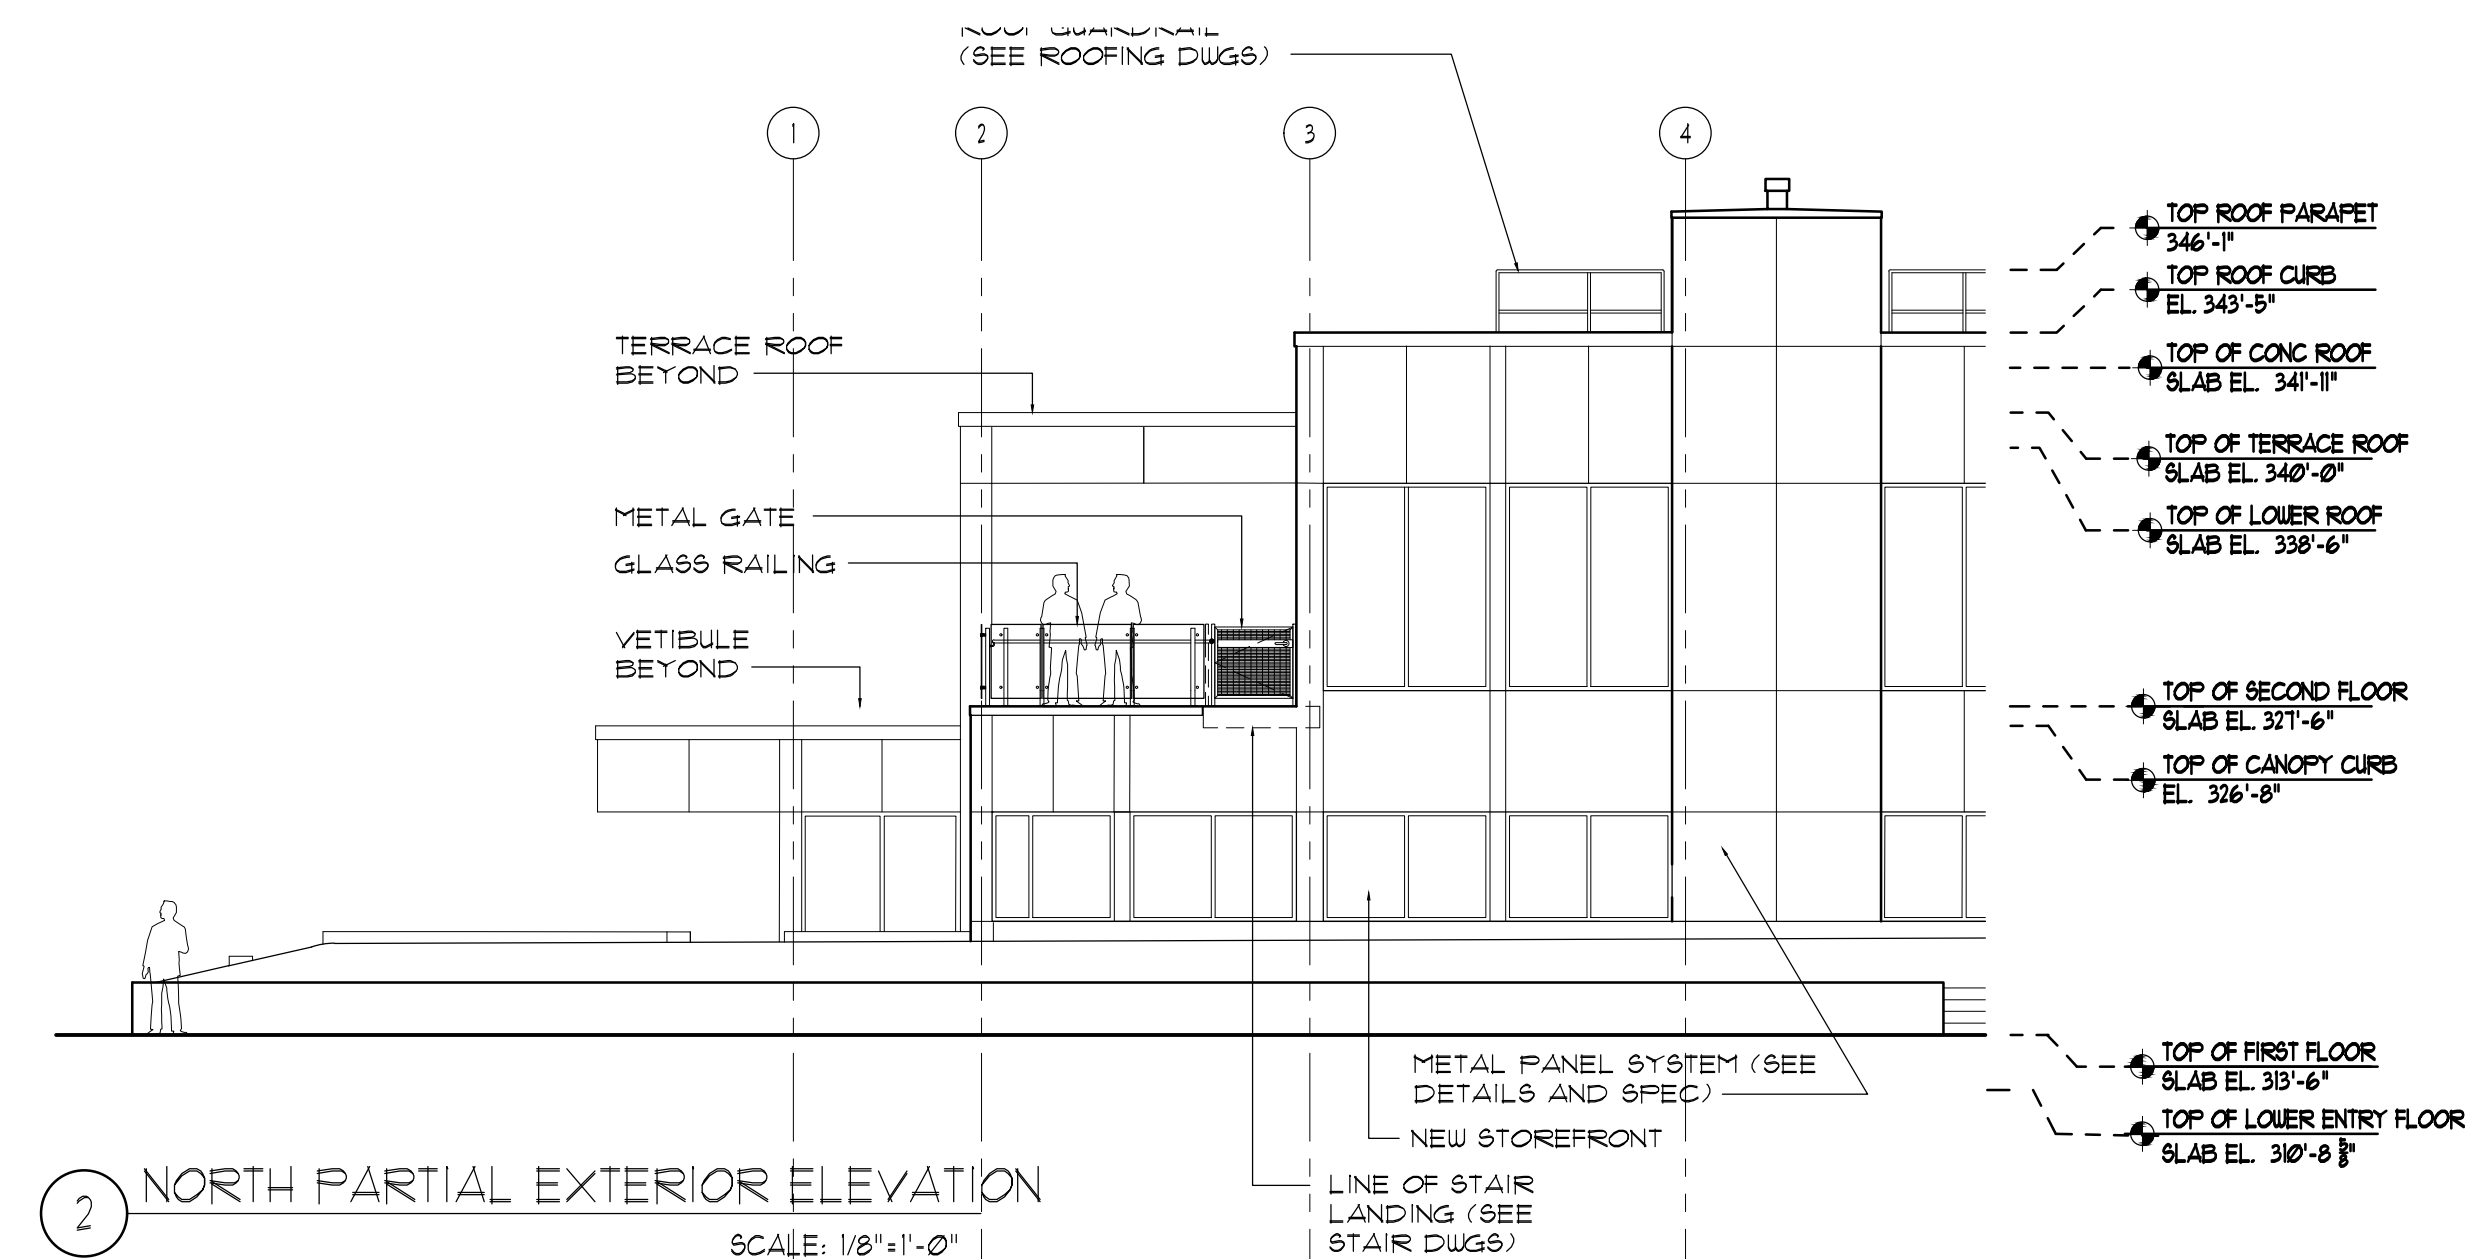


2 NORTH PARTIAL EXTERIOR ELEVATION
SCALE: 1/8"=1'-0"

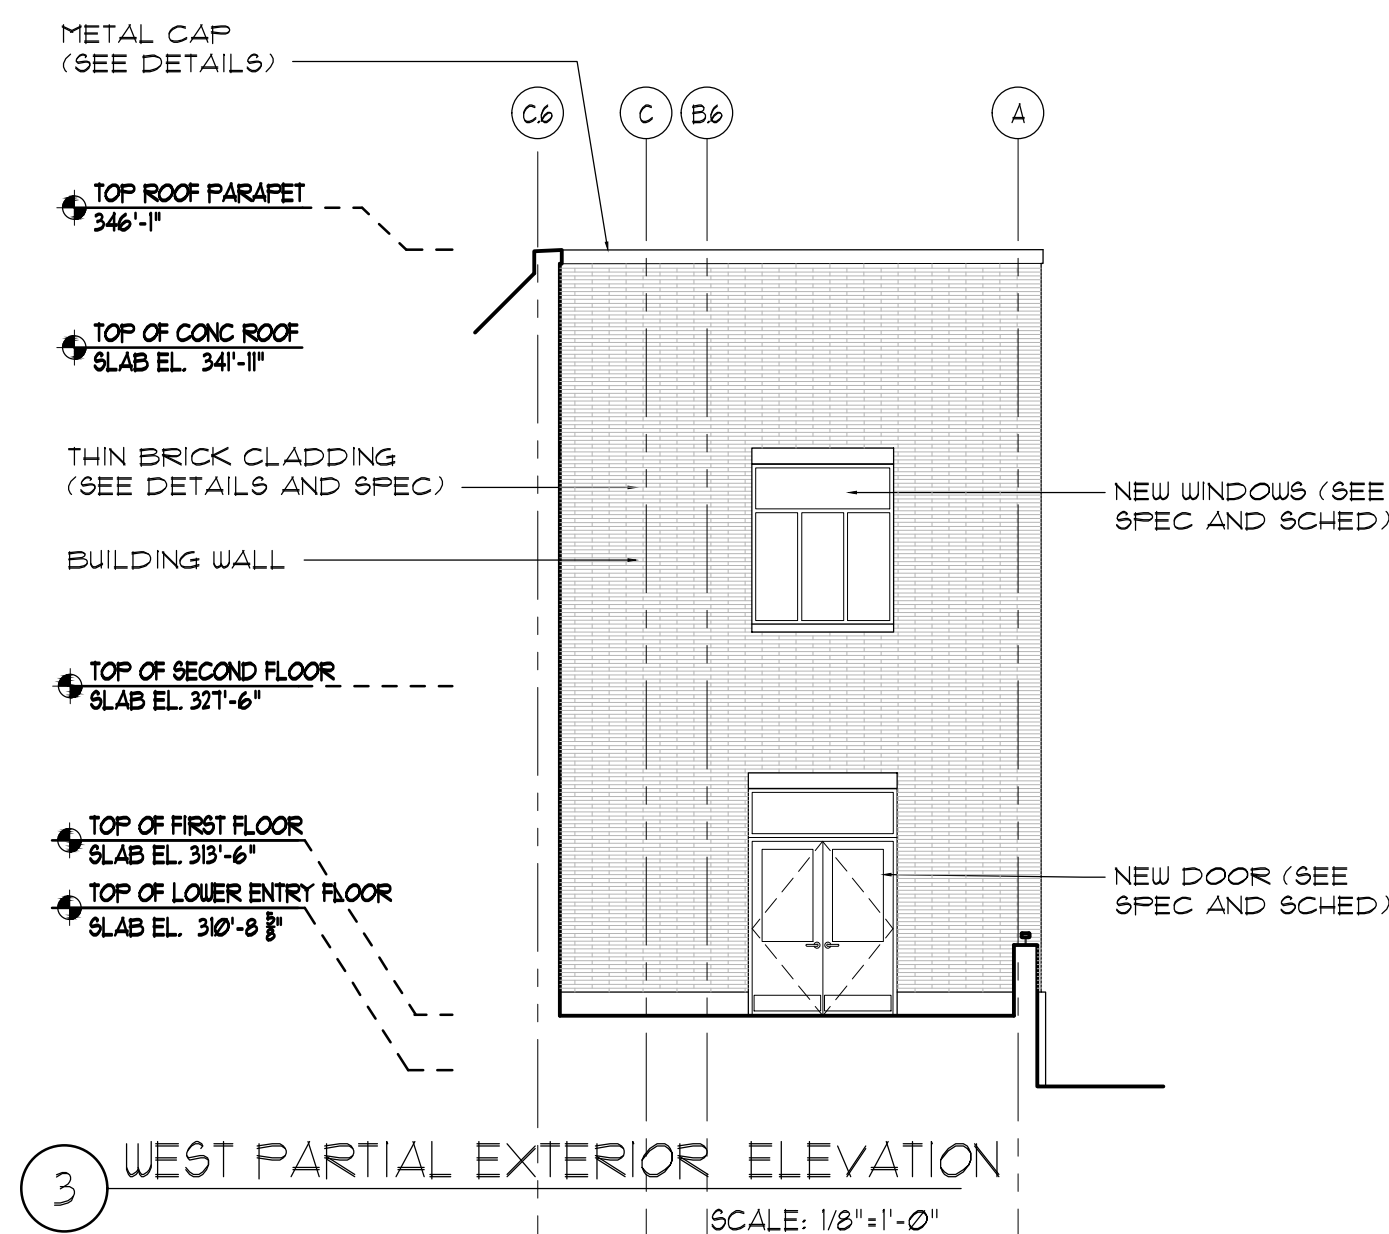

3 WEST PARTIAL EXTERIOR ELEVATION
SCALE: 1/8"=1'-0"

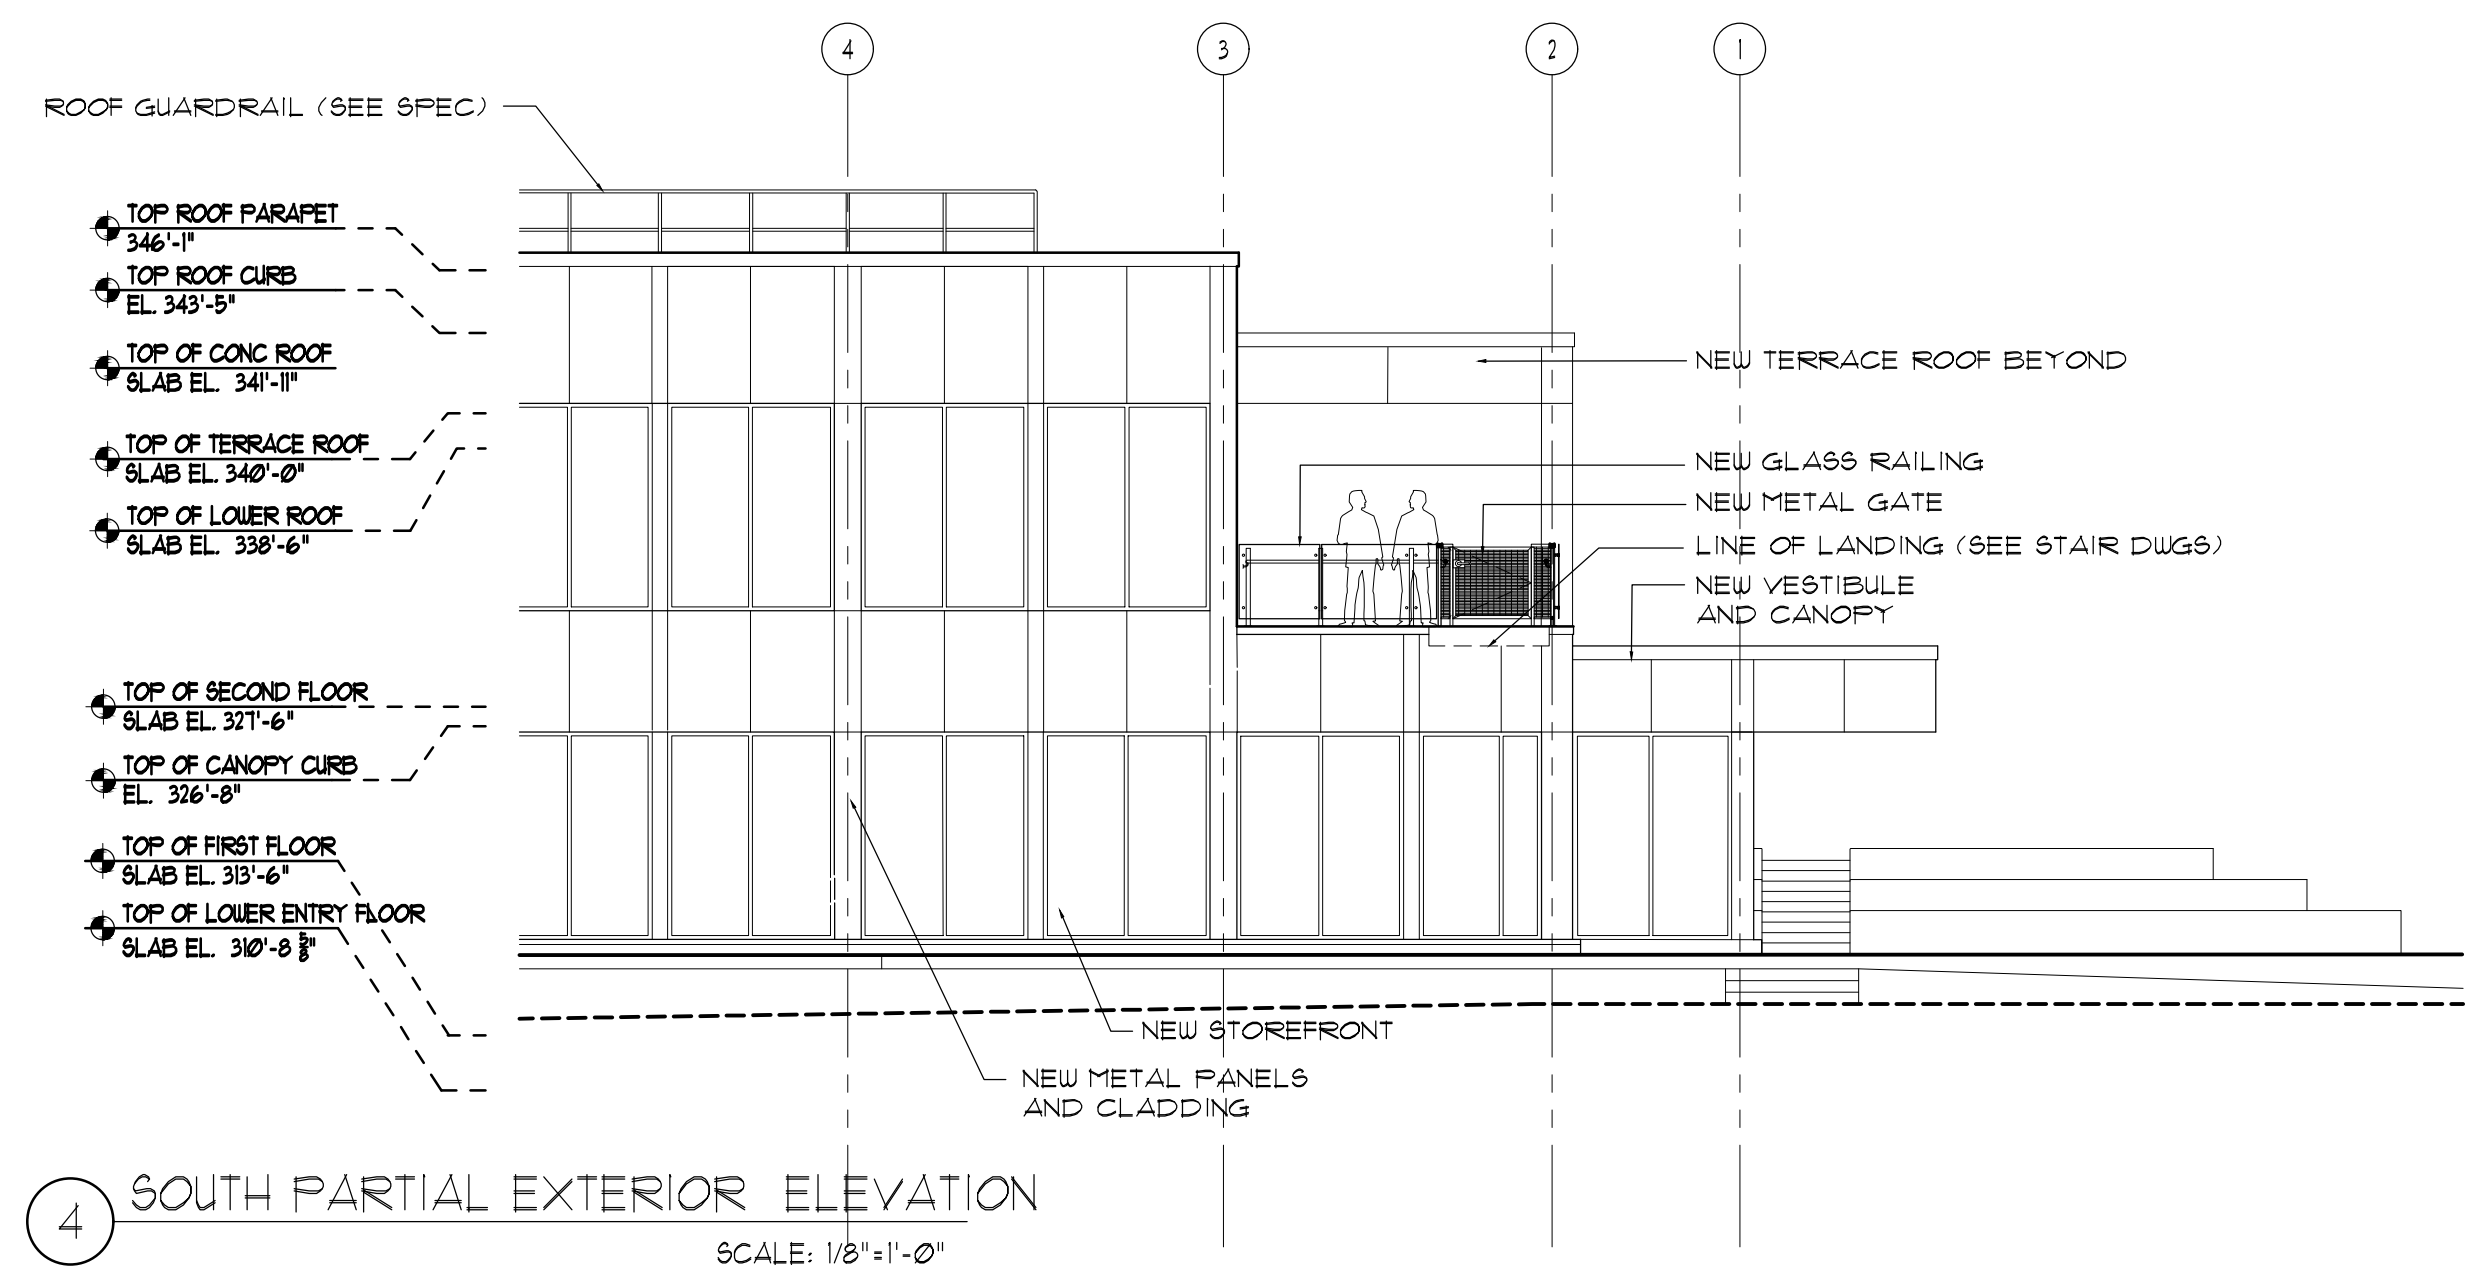

4 SOUTH PARTIAL EXTERIOR ELEVATION
SCALE: 1/8"=1'-0"

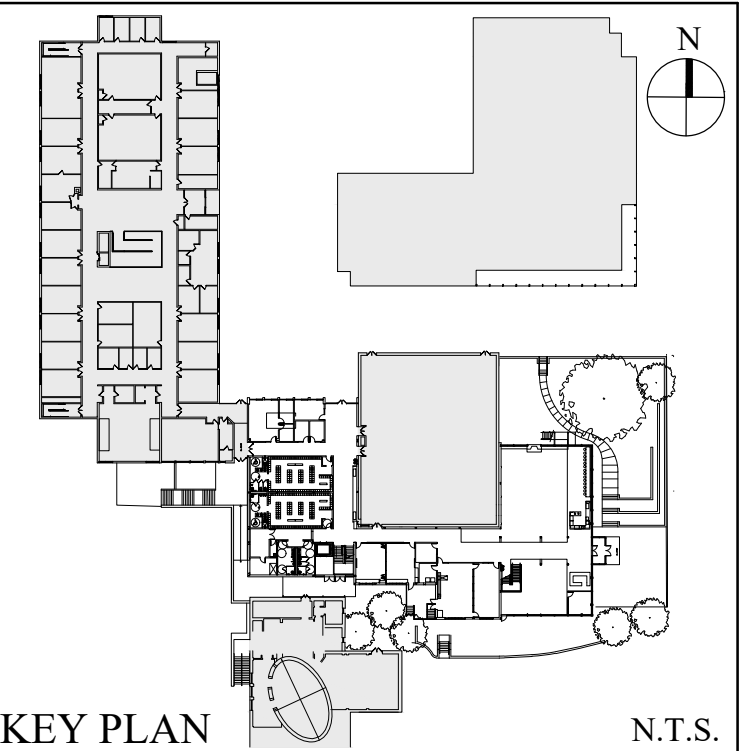

NOT FOR CONSTRUCTION

No.	Date	Revision
1.	08/29/2025	ZBA SUBMITTAL
ARCHITECT PETER GISOLFI ASSOCIATES, LLP 566 WARBURTON AVENUE HASTINGS-ON-HUDSON, NY 10706 T: (914) 478-3677 MEP ENGINEERS TETTER VENTURES, PLLC 68 PURCHASE STREET RYE, NY 10580 T: (914) 967-9509 CODE CONSULTANT MILTON GREGORY CREW, AIA 241 MAIN STREET SOUTH WOODBRURY, CT 06798 T: (203) 217-1074 GEOTECHNICAL ENGINEER (BY OWNER) LANGAN CT, INC. 555 LONG WHARF DRIVE NEW HAVEN, CT 06595 (203) 562-5771 STRUCTURAL ENGINEER DRPILLA CONSULTING ENGINEERS 143 MAIN STREET NYACK, NY 10960 T: (845) 927-7793 ROOFING CONSULTANT WATKINS ASSOCIATES 20 MADISON AVENUE VALHALLA, NY 10985 T: (914) 948-3450 SPECIFICATIONS CONSTRUCTION SPECIFICATIONS INC. PO BOX 488 MORGANVILLE, NJ 07751 T: (732) 970-0700 CIVIL ENGINEER (BY OWNER) RIDNESS AND MEAD 23 FIRST STREET STAMFORD, CT 06905 (203) 327-0500		

Project Title			
KING SCHOOL UPPER SCHOOL CRI/COMMONS ADDITION PROJECT 1450 Newfield Avenue Stamford, CT 06905			
Drawing Title			
UPPER SCHOOL EXTERIOR ELEVATIONS			
Scale	Job No.	Date	Drawing No.
	2301.00	02/2025	A-201
Drawn	Checked	Approved	
Peter Gisolfi Associates Architects • Landscape Architects, LLP 566 Warburton Avenue Hastings on Hudson, NY 10706 (914) 478-3677			
PETER GISOLFI ASSOCIATES LLP			