


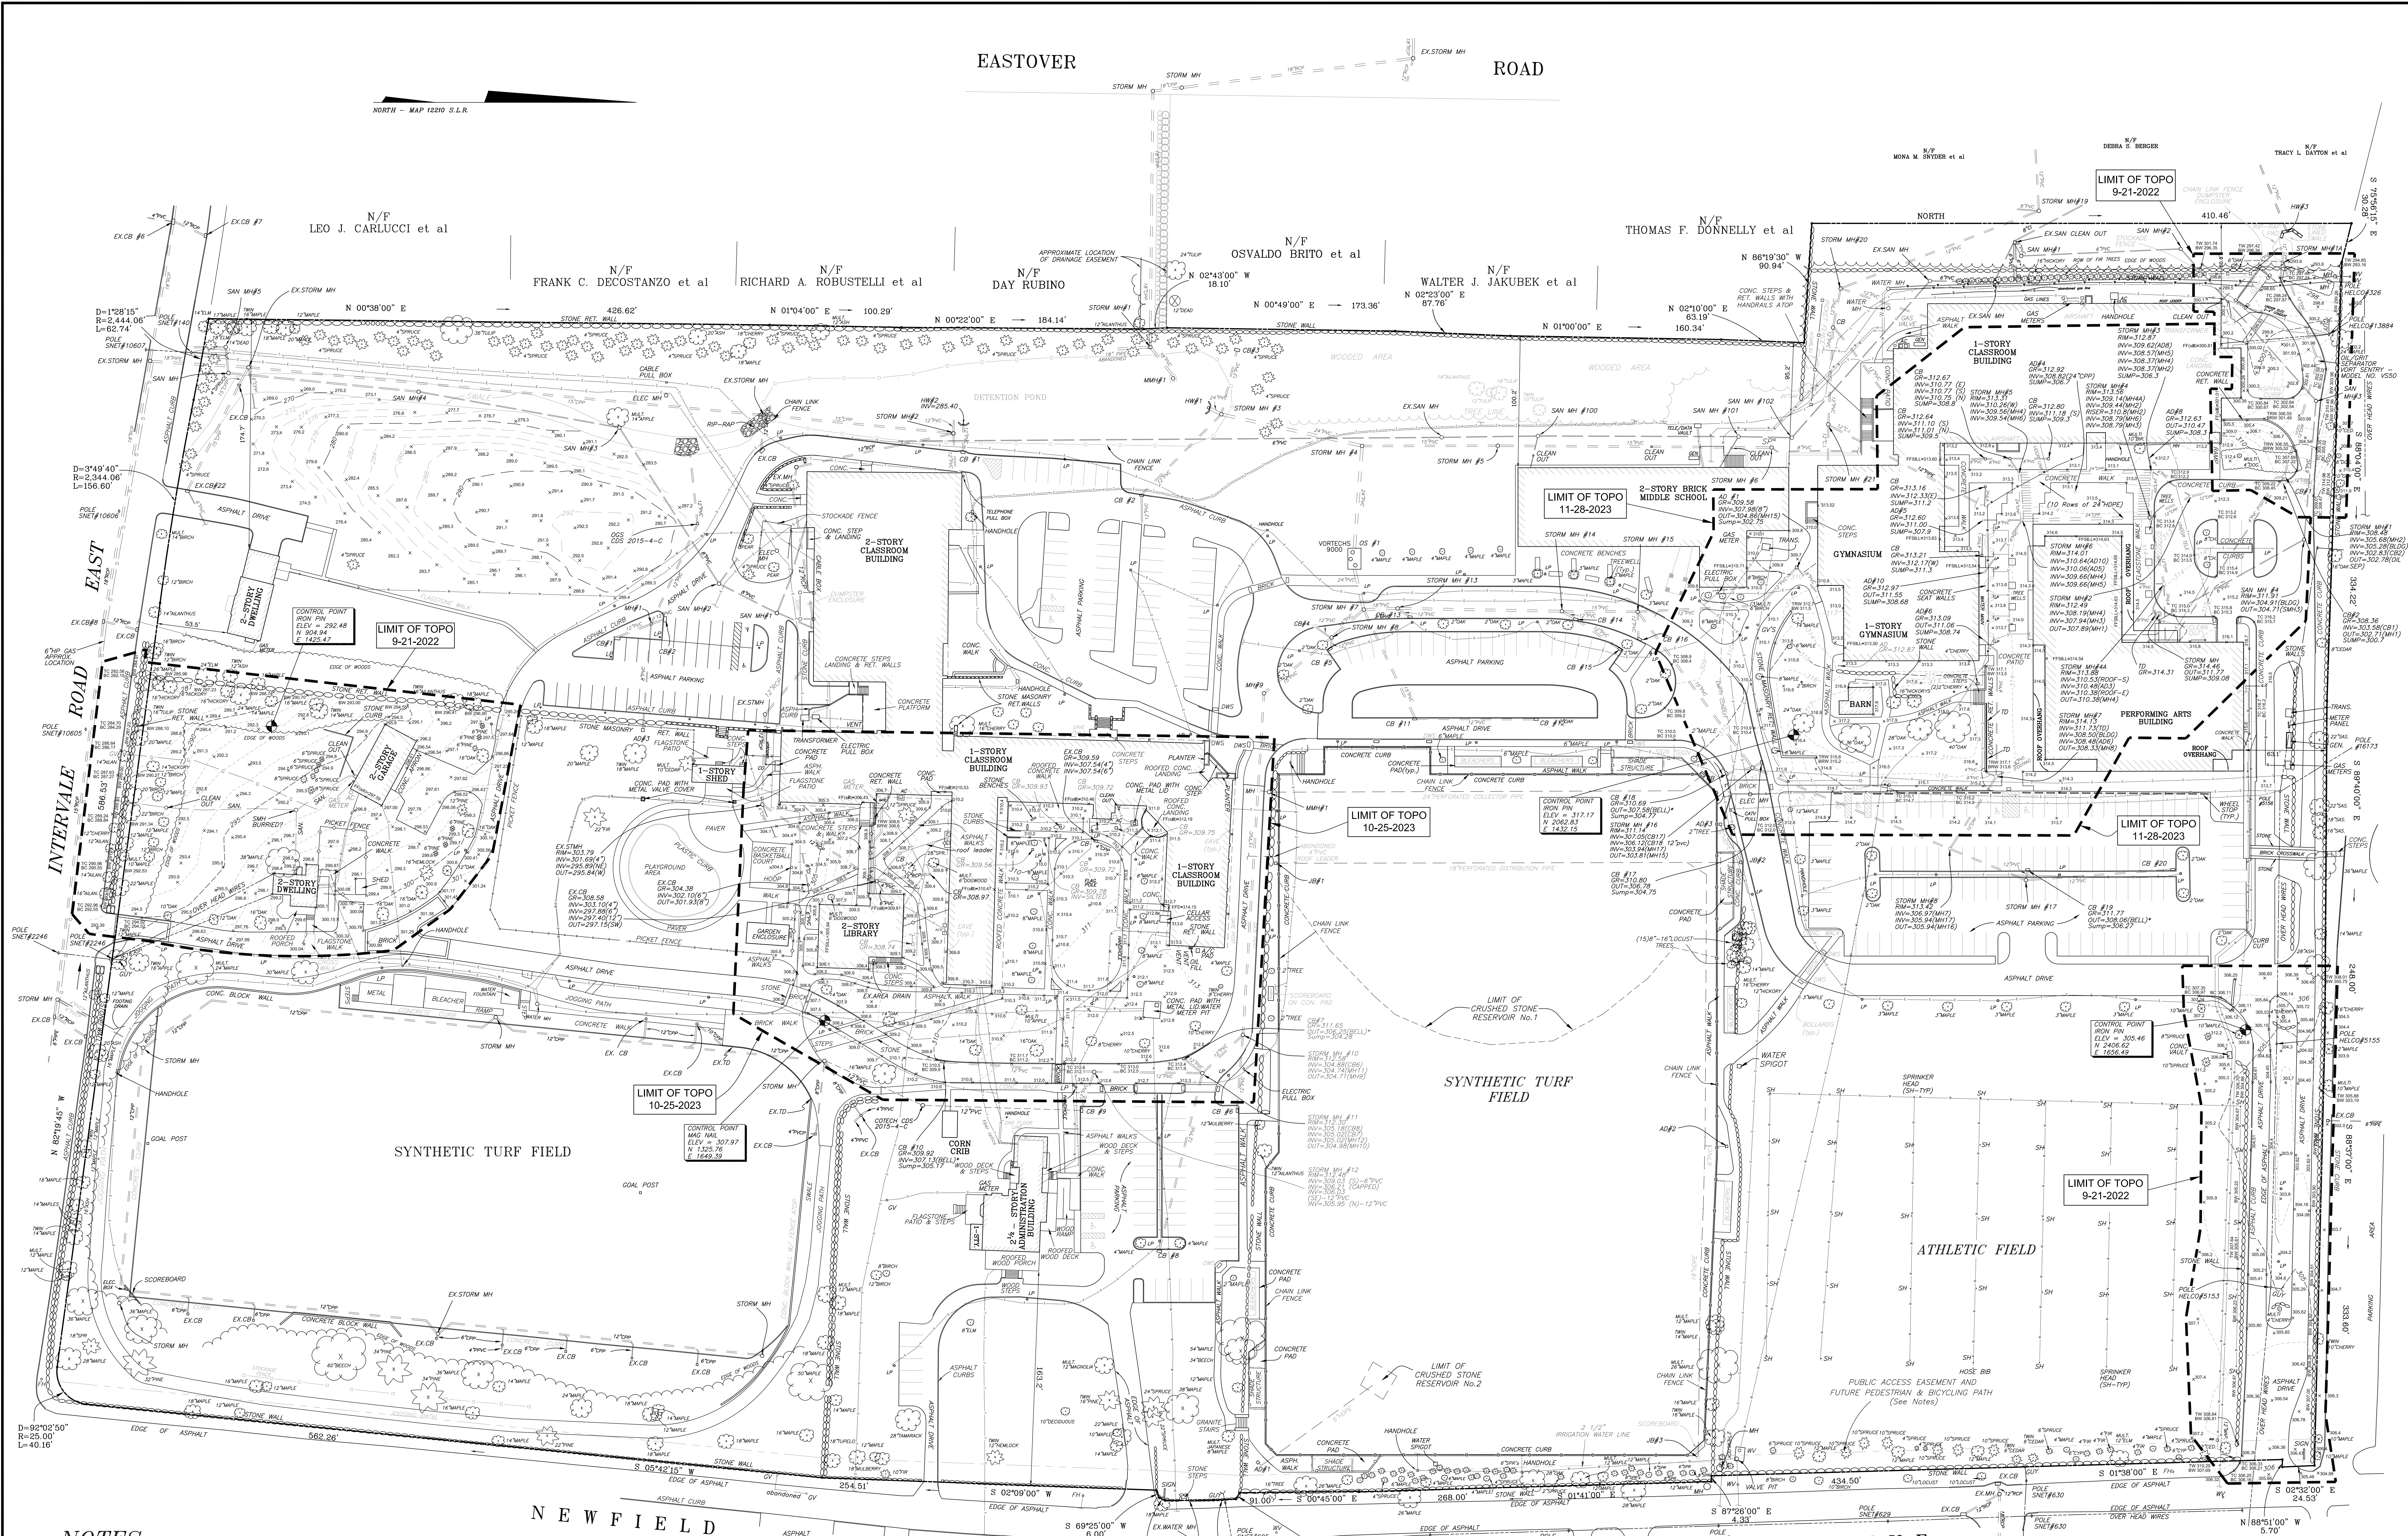

NOTES:

- This survey has been prepared in accordance with Sections 20-300b-1 thru 20-300b-20 of the Regulations of Connecticut State Agencies and the "Standards for Surveys and Maps in the State of Connecticut" as adopted by the Connecticut Association of Land Surveyors, Inc. as a Property & Limited Topographic Survey the Boundary Determination Category of which is a Resurvey conforming to Horizontal Accuracy Class A-2 and the locations and elevations of which conform to Topographic Accuracy Class T-2. It is intended to depict property boundaries, locations and elevations of improvements and topographic features.
- Reference is hereby made to the following maps of record: 7345, 8702, 9041, 10255 and Parcel A, Map 12210 in file in the Stamford Land Records.
- Reference is made to "Topographic Survey depicting 1450 Newfield Avenue, prepared for King School Stamford, CT", dated 4/17/2019 and prepared by this office.
- Total lot area = 1,483,209± SF or 34,0498 Ac.
- Elevations depicted hereon are based on the National Geodetic Vertical Datum of 1929 (NGVD-29).
- Reference is made to FEMA Flood Insurance Rate Map No. 09001C0506F, effective date June 18, 2010. Subject parcel does not lie within a Special Flood Hazard Area.
- Record owners: King School, Inc.
- Subsurface utility, structure and facility locations depicted hereon have been compiled, in part, from municipal records, field measurements and contractor's records. These locations must be considered as approximate, may not be complete and other such features may exist on the site. The size, location and existence of all such features must be verified by the appropriate authorities prior to construction.

PROPERTY & LIMITED
TOPOGRAPHIC SURVEY
DEPICTING
1450 NEWFIELD AVENUE
STAMFORD, CT
PREPARED FOR
KING SCHOOL



LAND SURVEYING
CIVIL ENGINEERING
PLANNING & ZONING CONSULTING
PERMITTING

To my knowledge and belief this map was substantially
correct as prepared from
DATE
12/15/2023

12/15/2023
12/15/2023
12/15/2023

Sheet No:
PLTS
Comm No: 3070-35

No.	Date	Revision Note
1	12/15/2023	Topographic areas added from 10/20/2023 & 11/28/2023.
No.	By	Date

12/14/2023 8:37 AM
C:\PROJECTS\3070-35\3070-35\Drawings\Survey\3070-35\12/15/2023 8:37 AM